

PLAN 3

RIGHT EXTERIOR ELEVATION 1/4" SCALE | 2



PLAN 1

PLAN 3

FRONT EXTERIOR ELEVATION 1/4" SCALE | 1

SCALE 3

NG DIM - U.N.O.

RAKE

0" 0'-6"

NT BY O'HAGIN
ATION
R MODEL/SIZE)

BY ART'S SHEET
ER DETAIL X/DX.X
ATION
R MODEL/SIZE)

ENT BY C & J
INC. - REFER
ATION
R MODEL/SIZE)

ECIFICATIONS.

WHERE THE

NTILATION -

INSTALLER.

KEYNO
668
701

WI
RO

1.
CLAS
2.
COM
AIRS
COM

ROO
BE IN
REQ
OR C
THE

THE

PREV
3.
TEST
E108
INST
INST
504.
RETA
COM
THE
CLAS
4.
THA
RESI
UND
SUR
OF T
5.
SOFF
CWU
6.
UNE
SECT
7.
NON
APPI
DEBI
8.
WILD
LIST
TEST
504.
9.
VENT
VENT
10.
INFO

IN ORD
THE AE
RESIDE
THE FO
PROTE

1.

2.

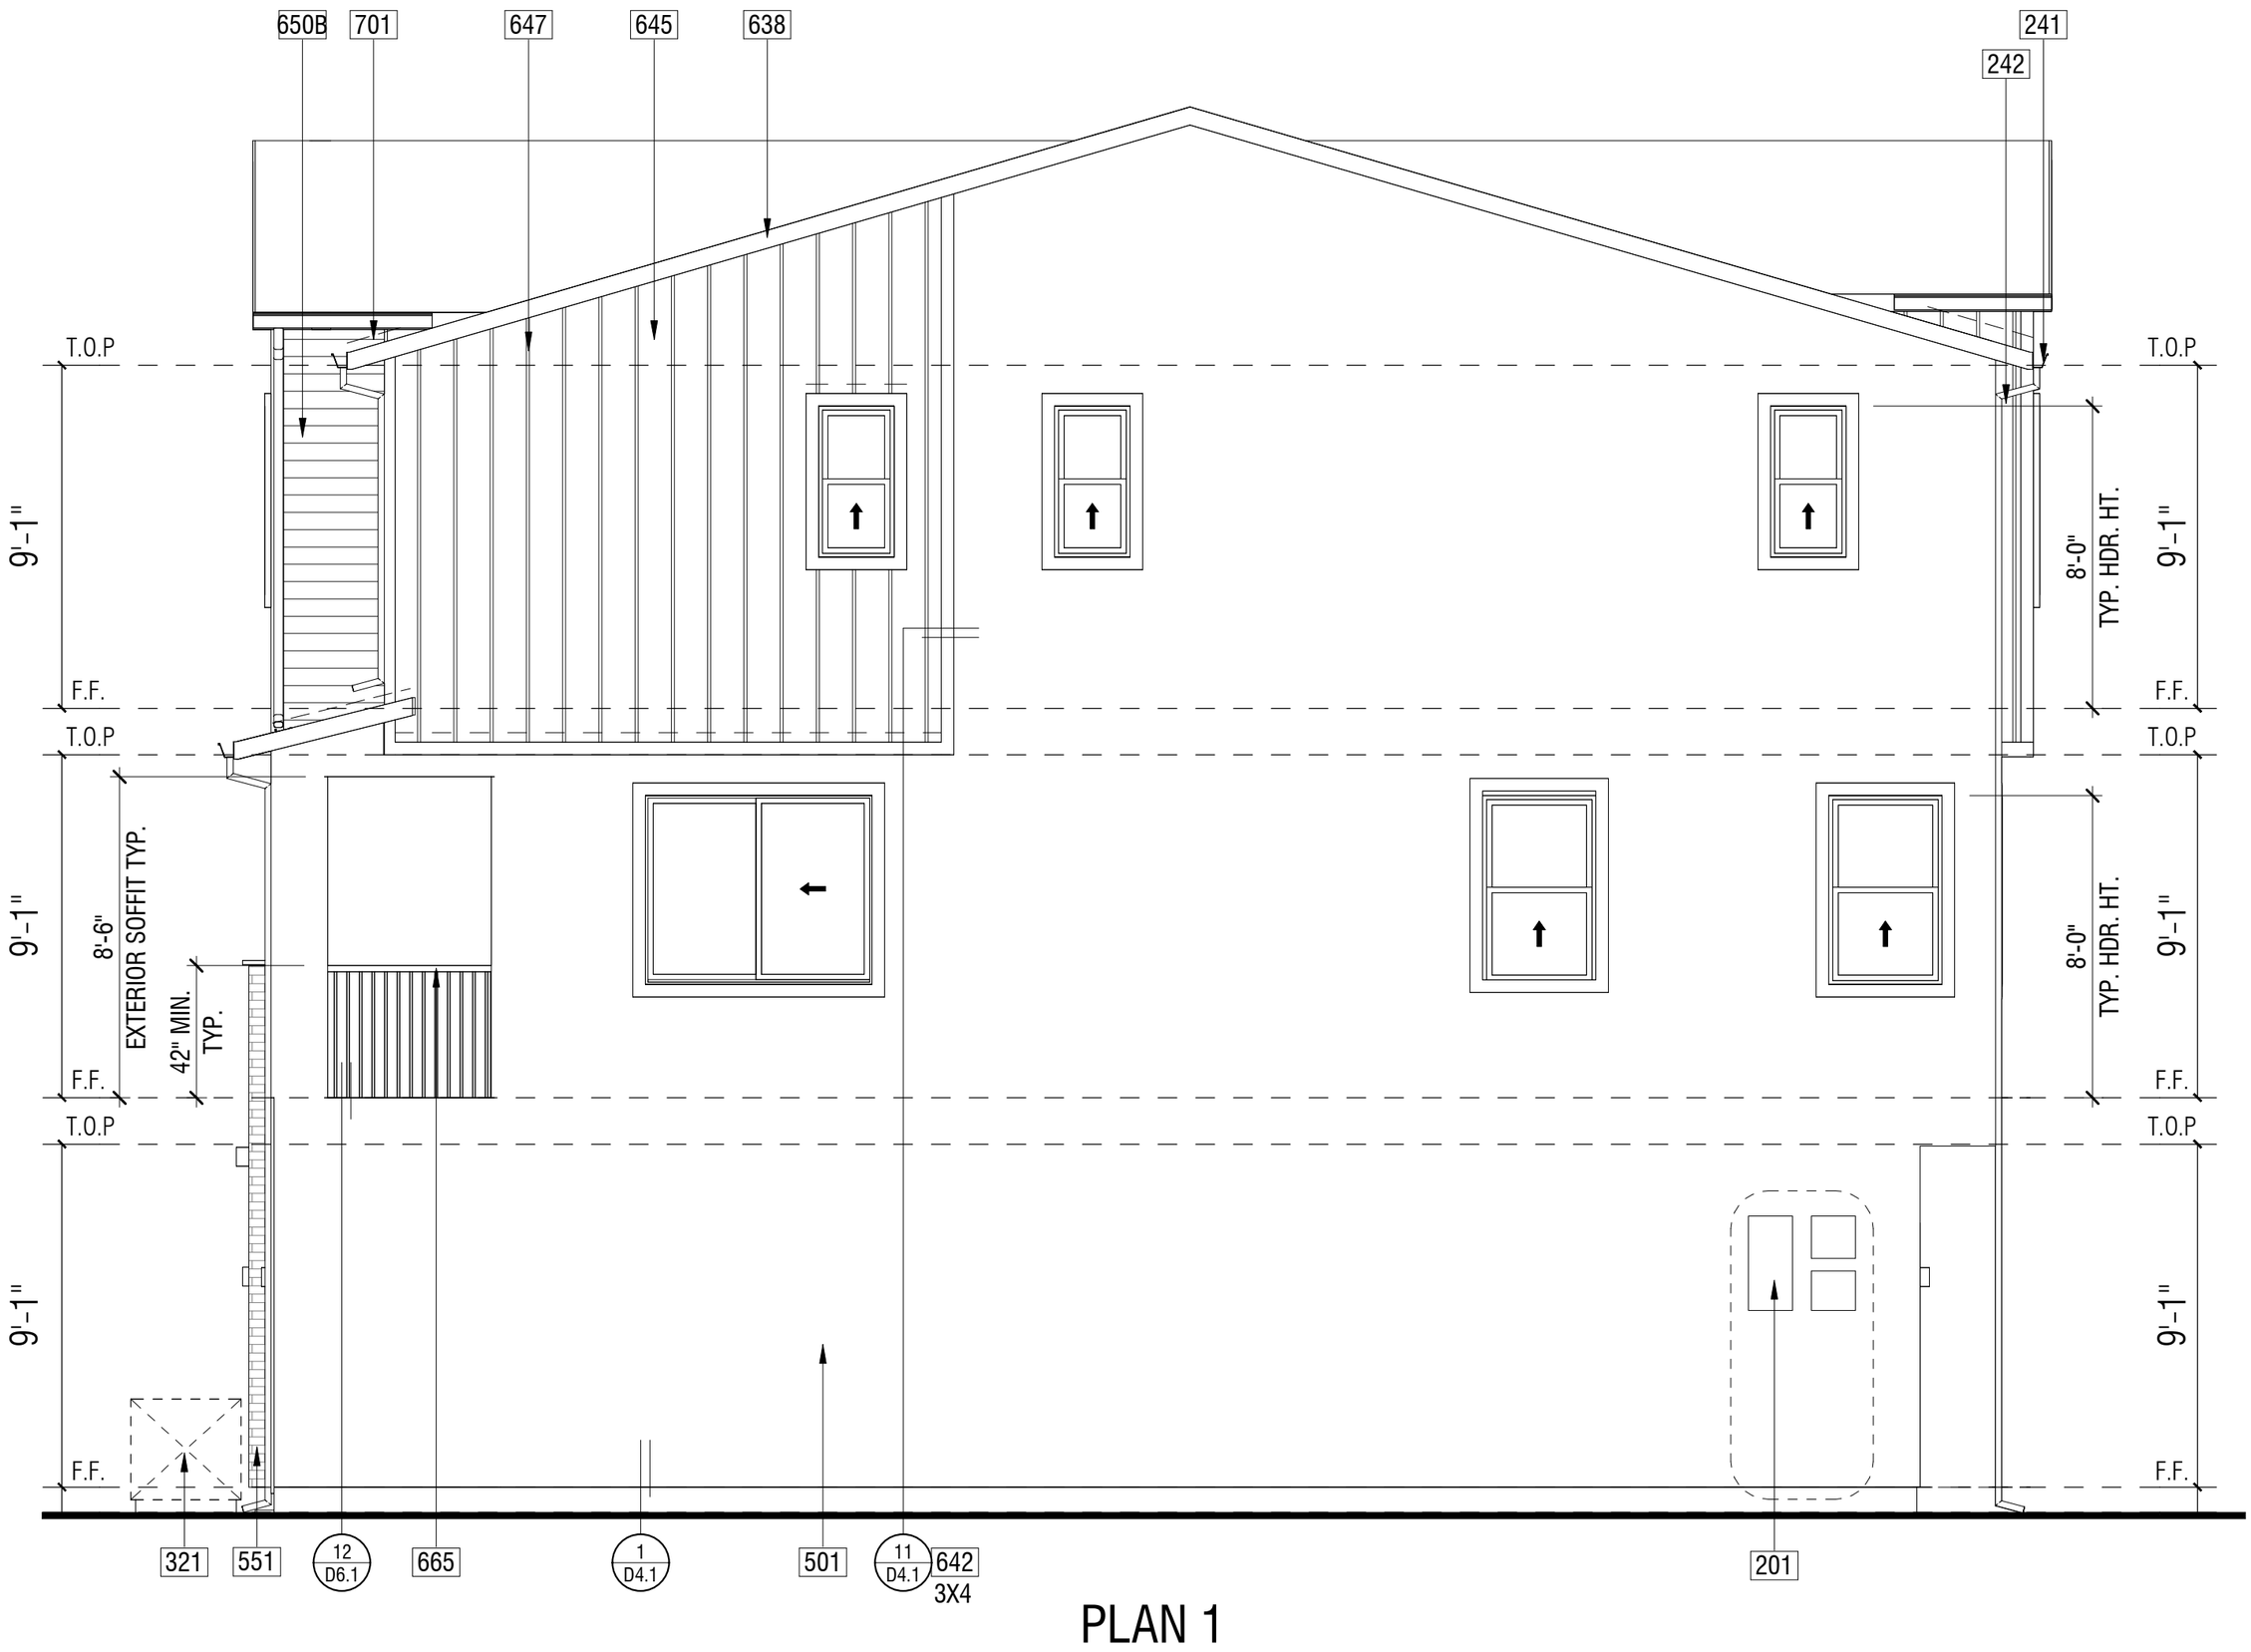
THE BU
STRUC

BUILDI
BUILDI
BUILDI
BUILDI

THE BU
REQUIR
SPECIF

BALC

BUILD
BUILD
BUILD
BUILD
BUILD
BUILD
BUILD
BUILD



PLAN 1

LEFT EXTERIOR ELEVATION 1/4" SCALE | 2



PLAN 3 PLAN 1

REAR EXTERIOR ELEVATION 1/4" SCALE | 1

WI
RO

1.
CLAS
2.
COM
AIRS
COM

ROO
BE IN
REQ
OR C
THE

THE

PREV
3.
TEST
E108
INST
INST
504.
RETA
COM
THE
CLAS
4.
THAI
RESI
UND
SUR
OF T
5.
SOFI
CWU
6.
UNE
SECT
7.
NON
APPI
DEBI
8.
WILD
LIST
TEST
504.
9.
VENT
VENT
10.
INFO

IN ORD
THE AE
RESIDE
THE FO
PROTE

1.

2.

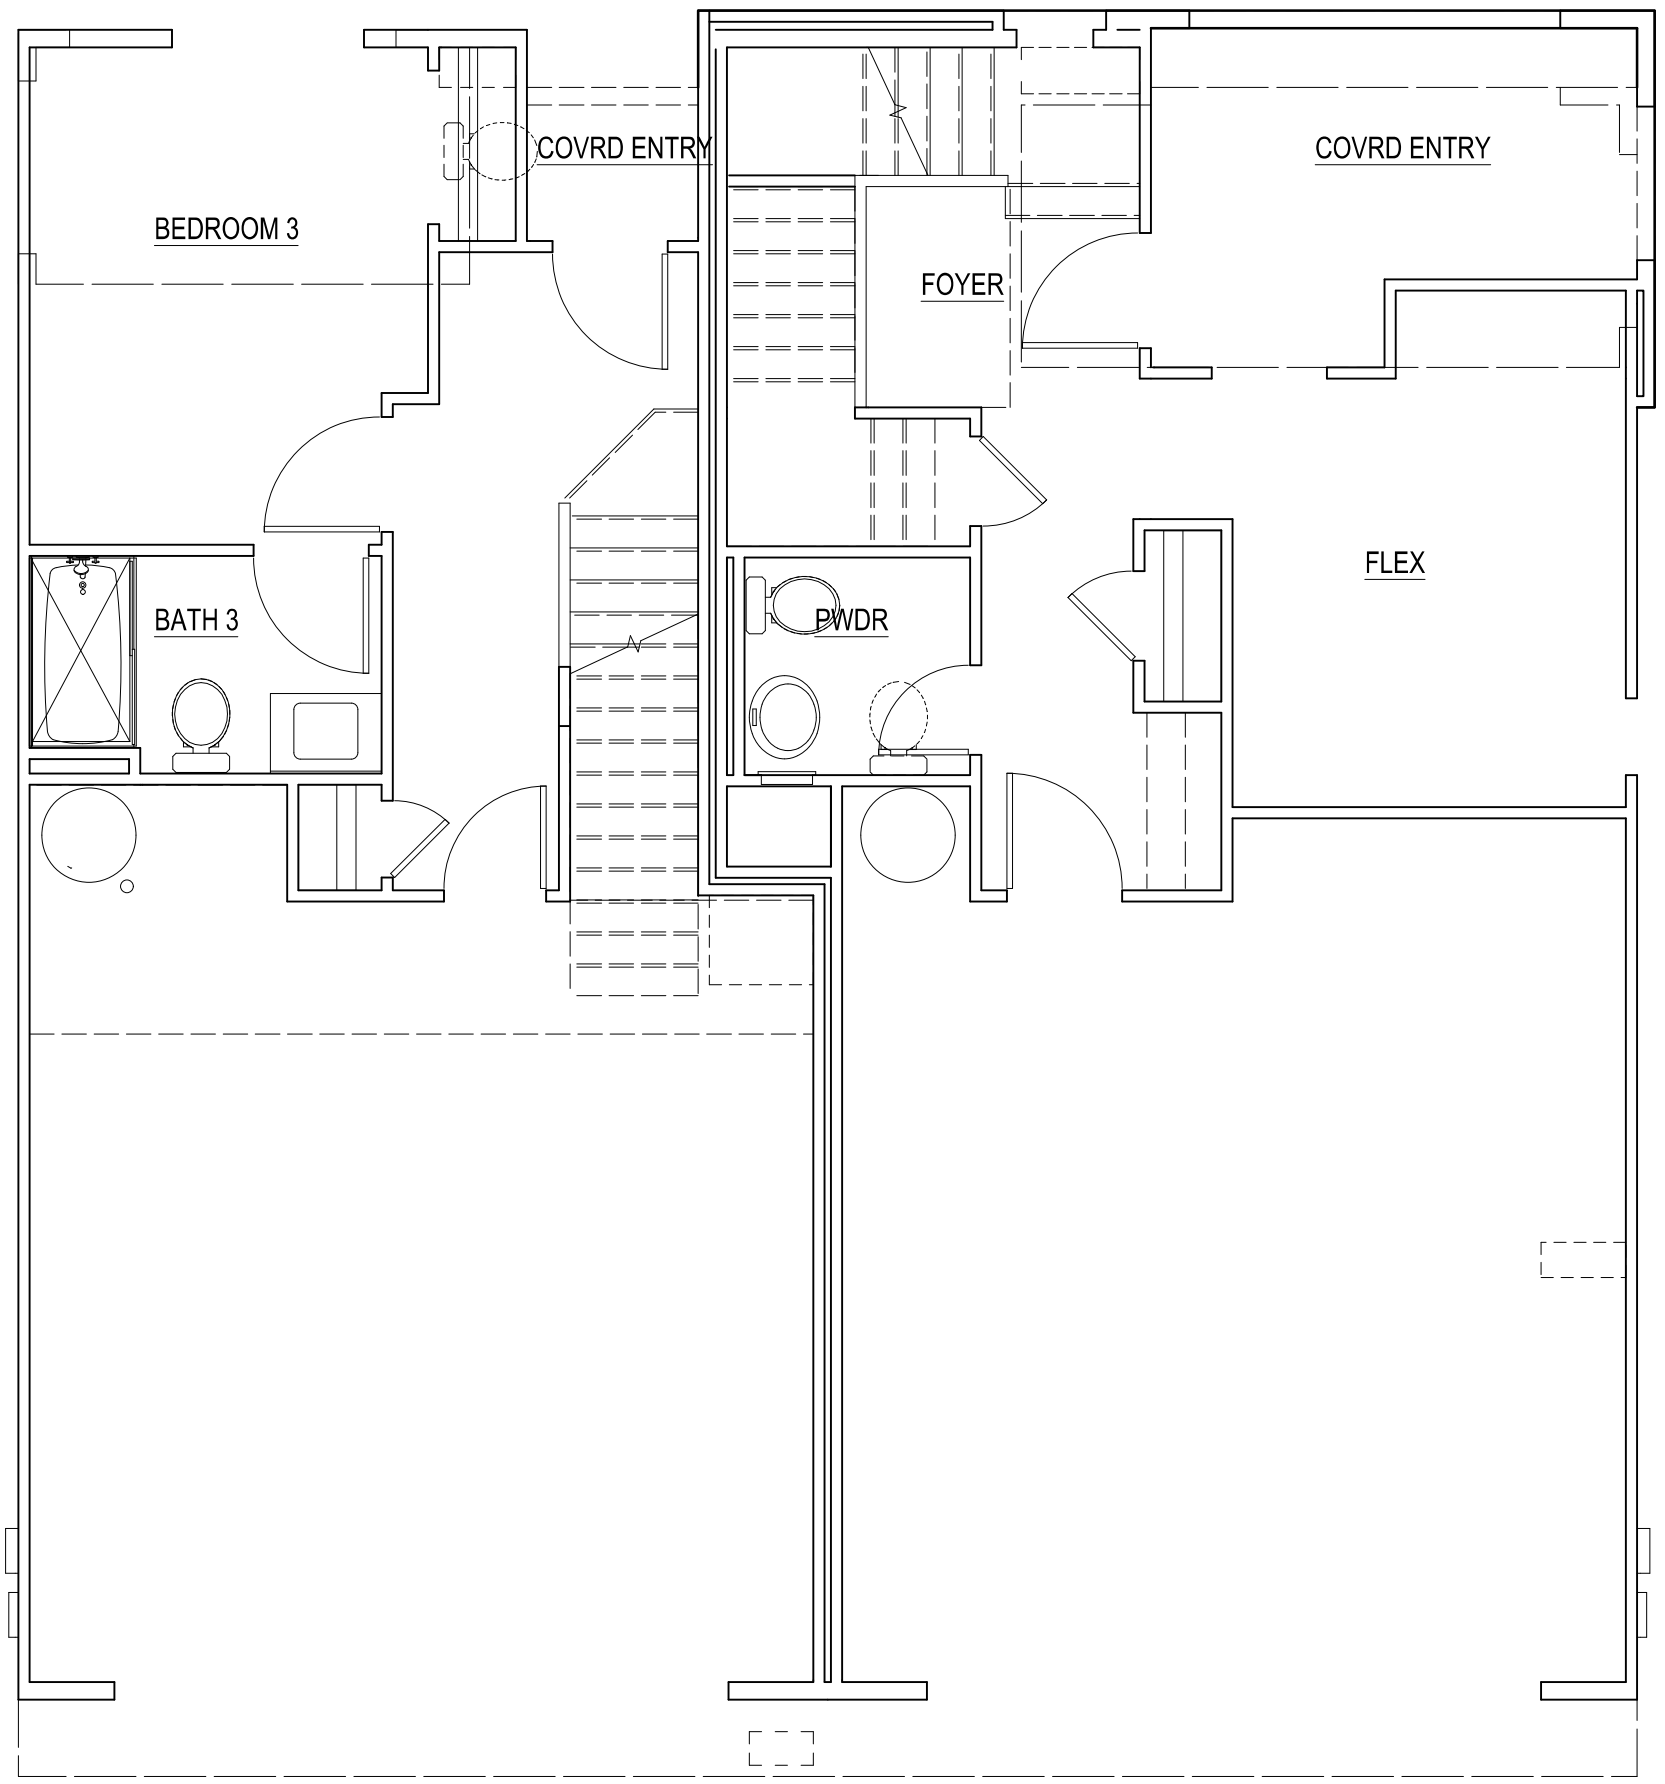
THE BU
STRUC

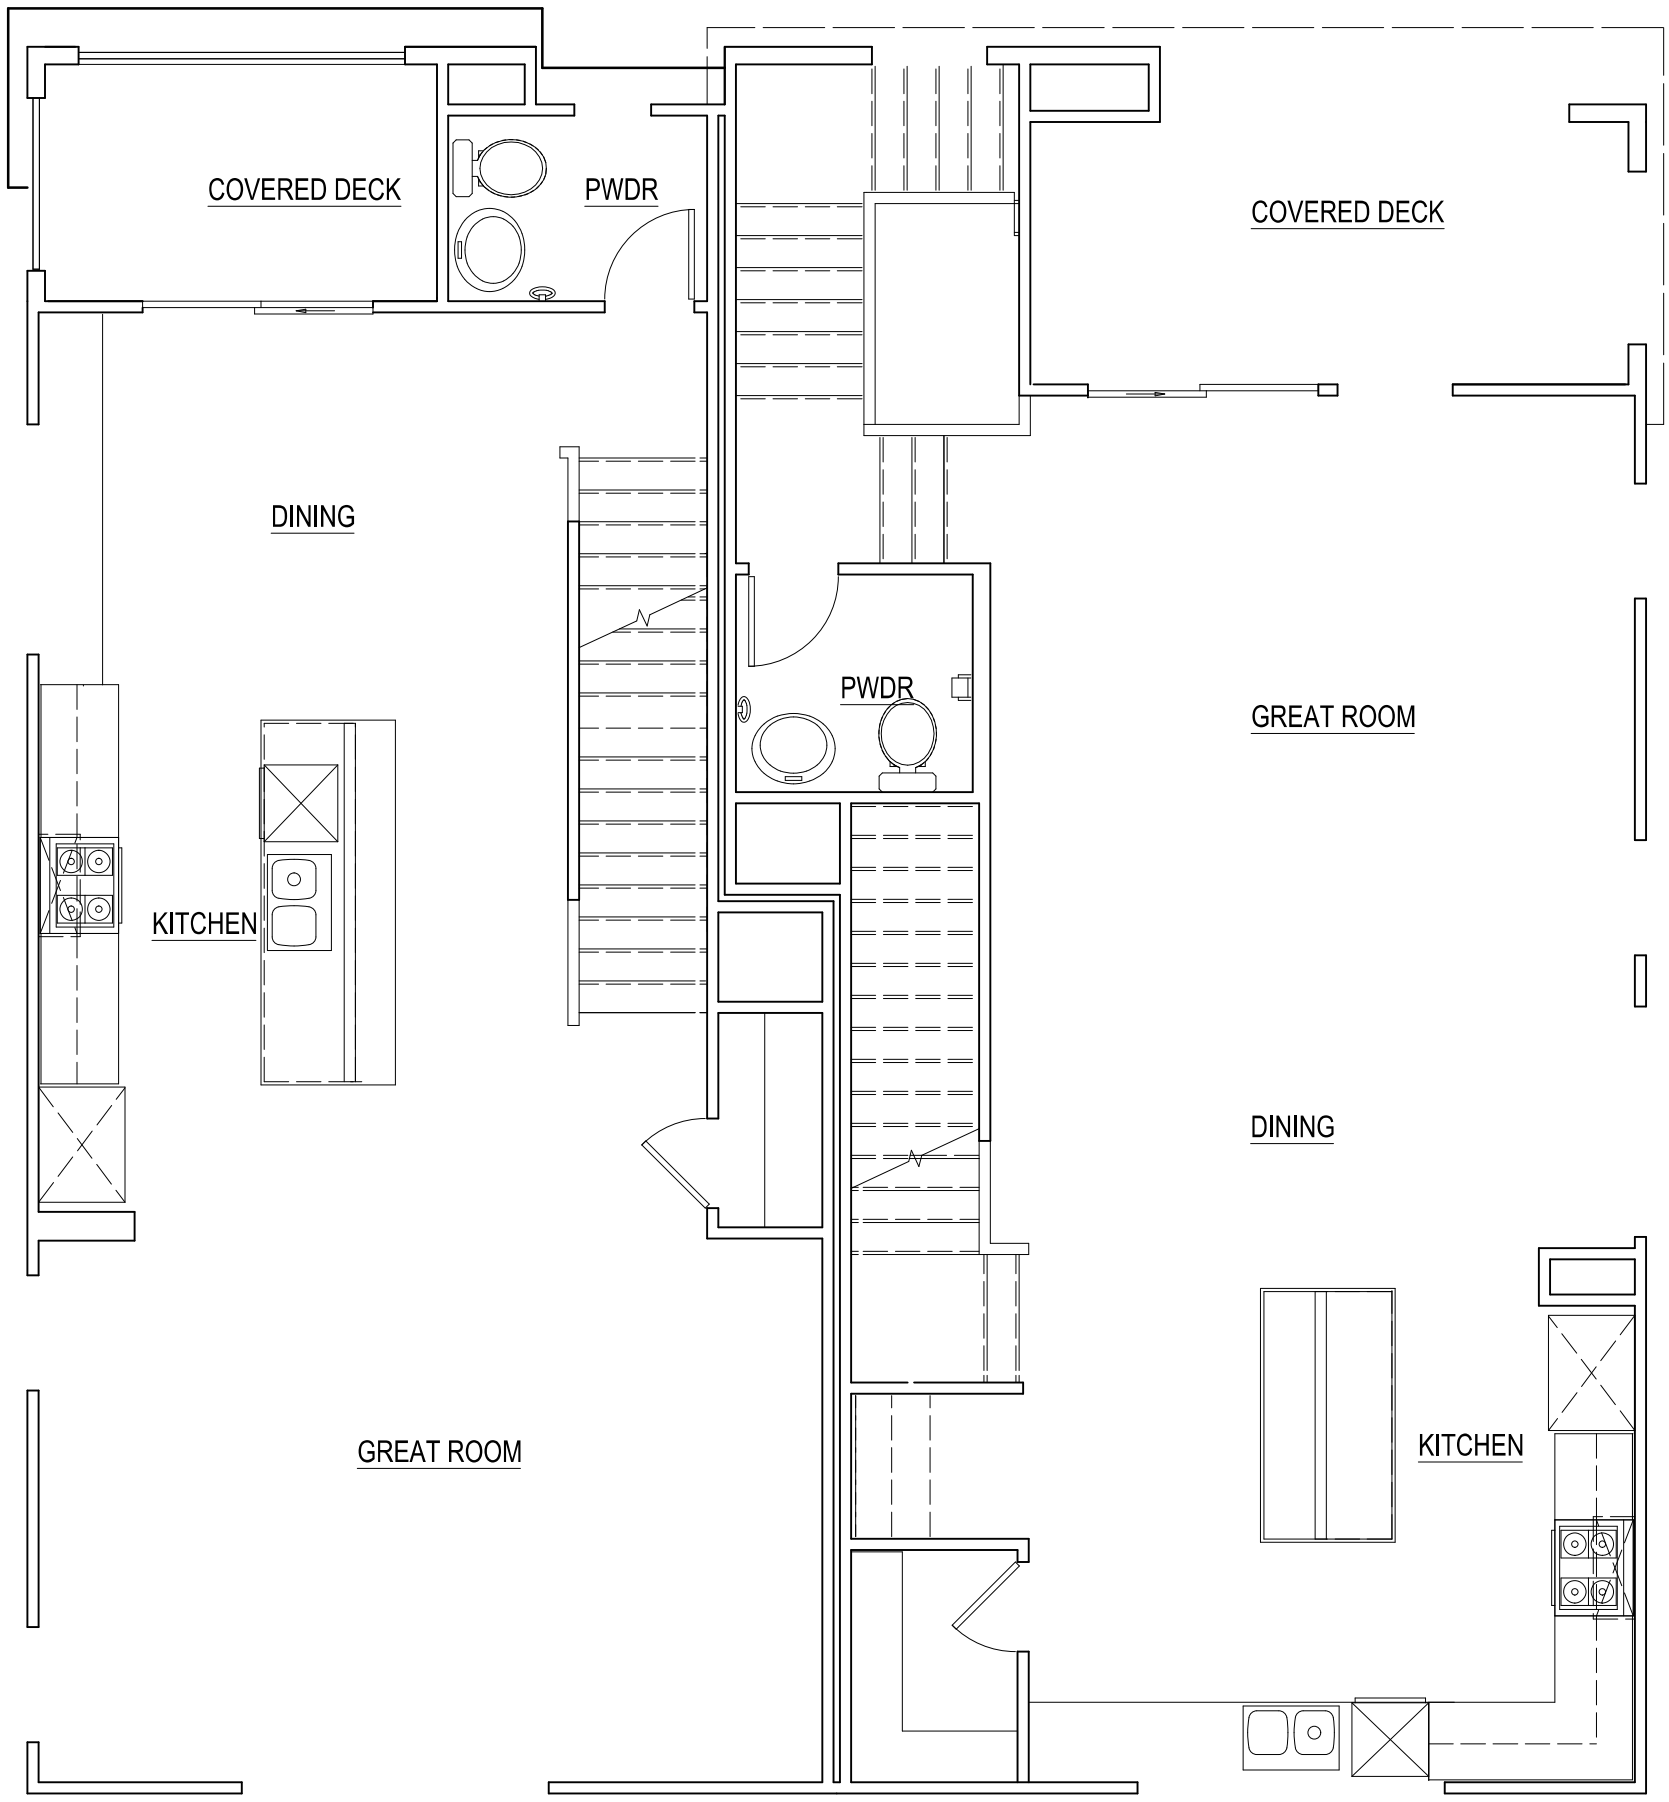
BUILDI
BUILDI
BUILDI
BUILDI

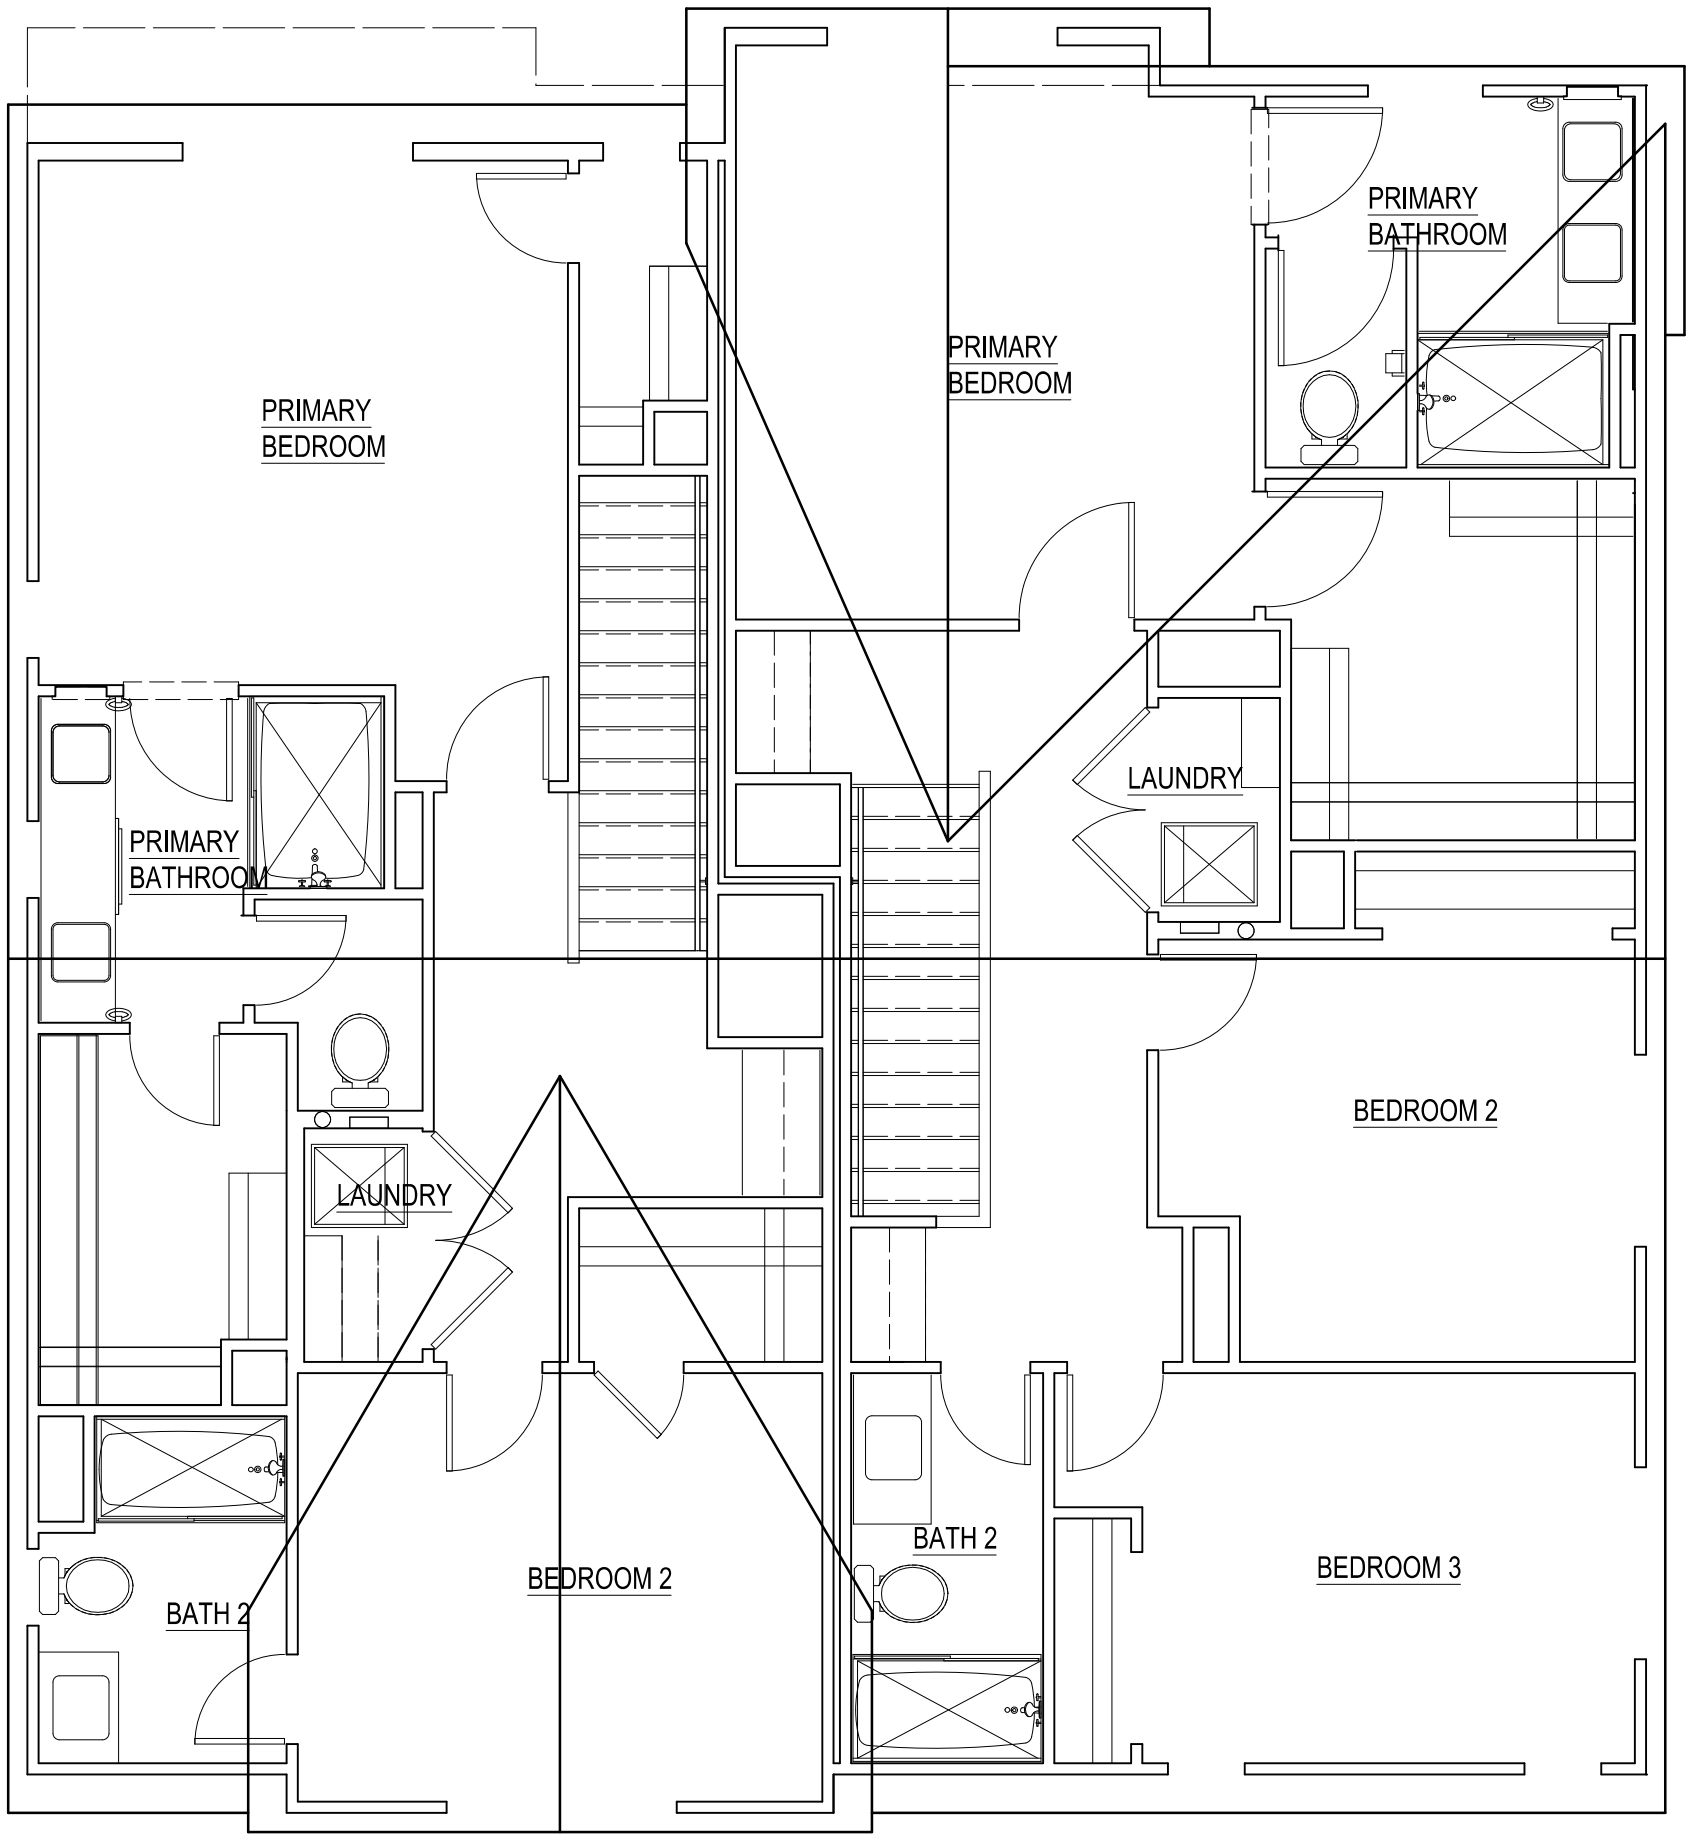
THE BU
REQUIR
SPECIF

BALC

BUILD
BUILD
BUILD
BUILD
BUILD
BUILD
BUILD
BUILD


COVRD ENTRY
COVRD ENTRY
BEDROOM 3
FOYER
FLEX
BATH 3
PWDR


COVERED DECK
PWDR
COVERED DECK
DINING
PWDR
GREAT ROOM
KITCHEN
DINING
GREAT ROOM
KITCHEN


PRIMARY
BEDROOM
PRIMARY
BATHROOM
PRIMARY
BEDROOM
LAUNDRY
PRIMARY
BATHROOM
LAUNDRY
BEDROOM 2
BATH 2
BEDROOM 2
BATH 2
BEDROOM 3